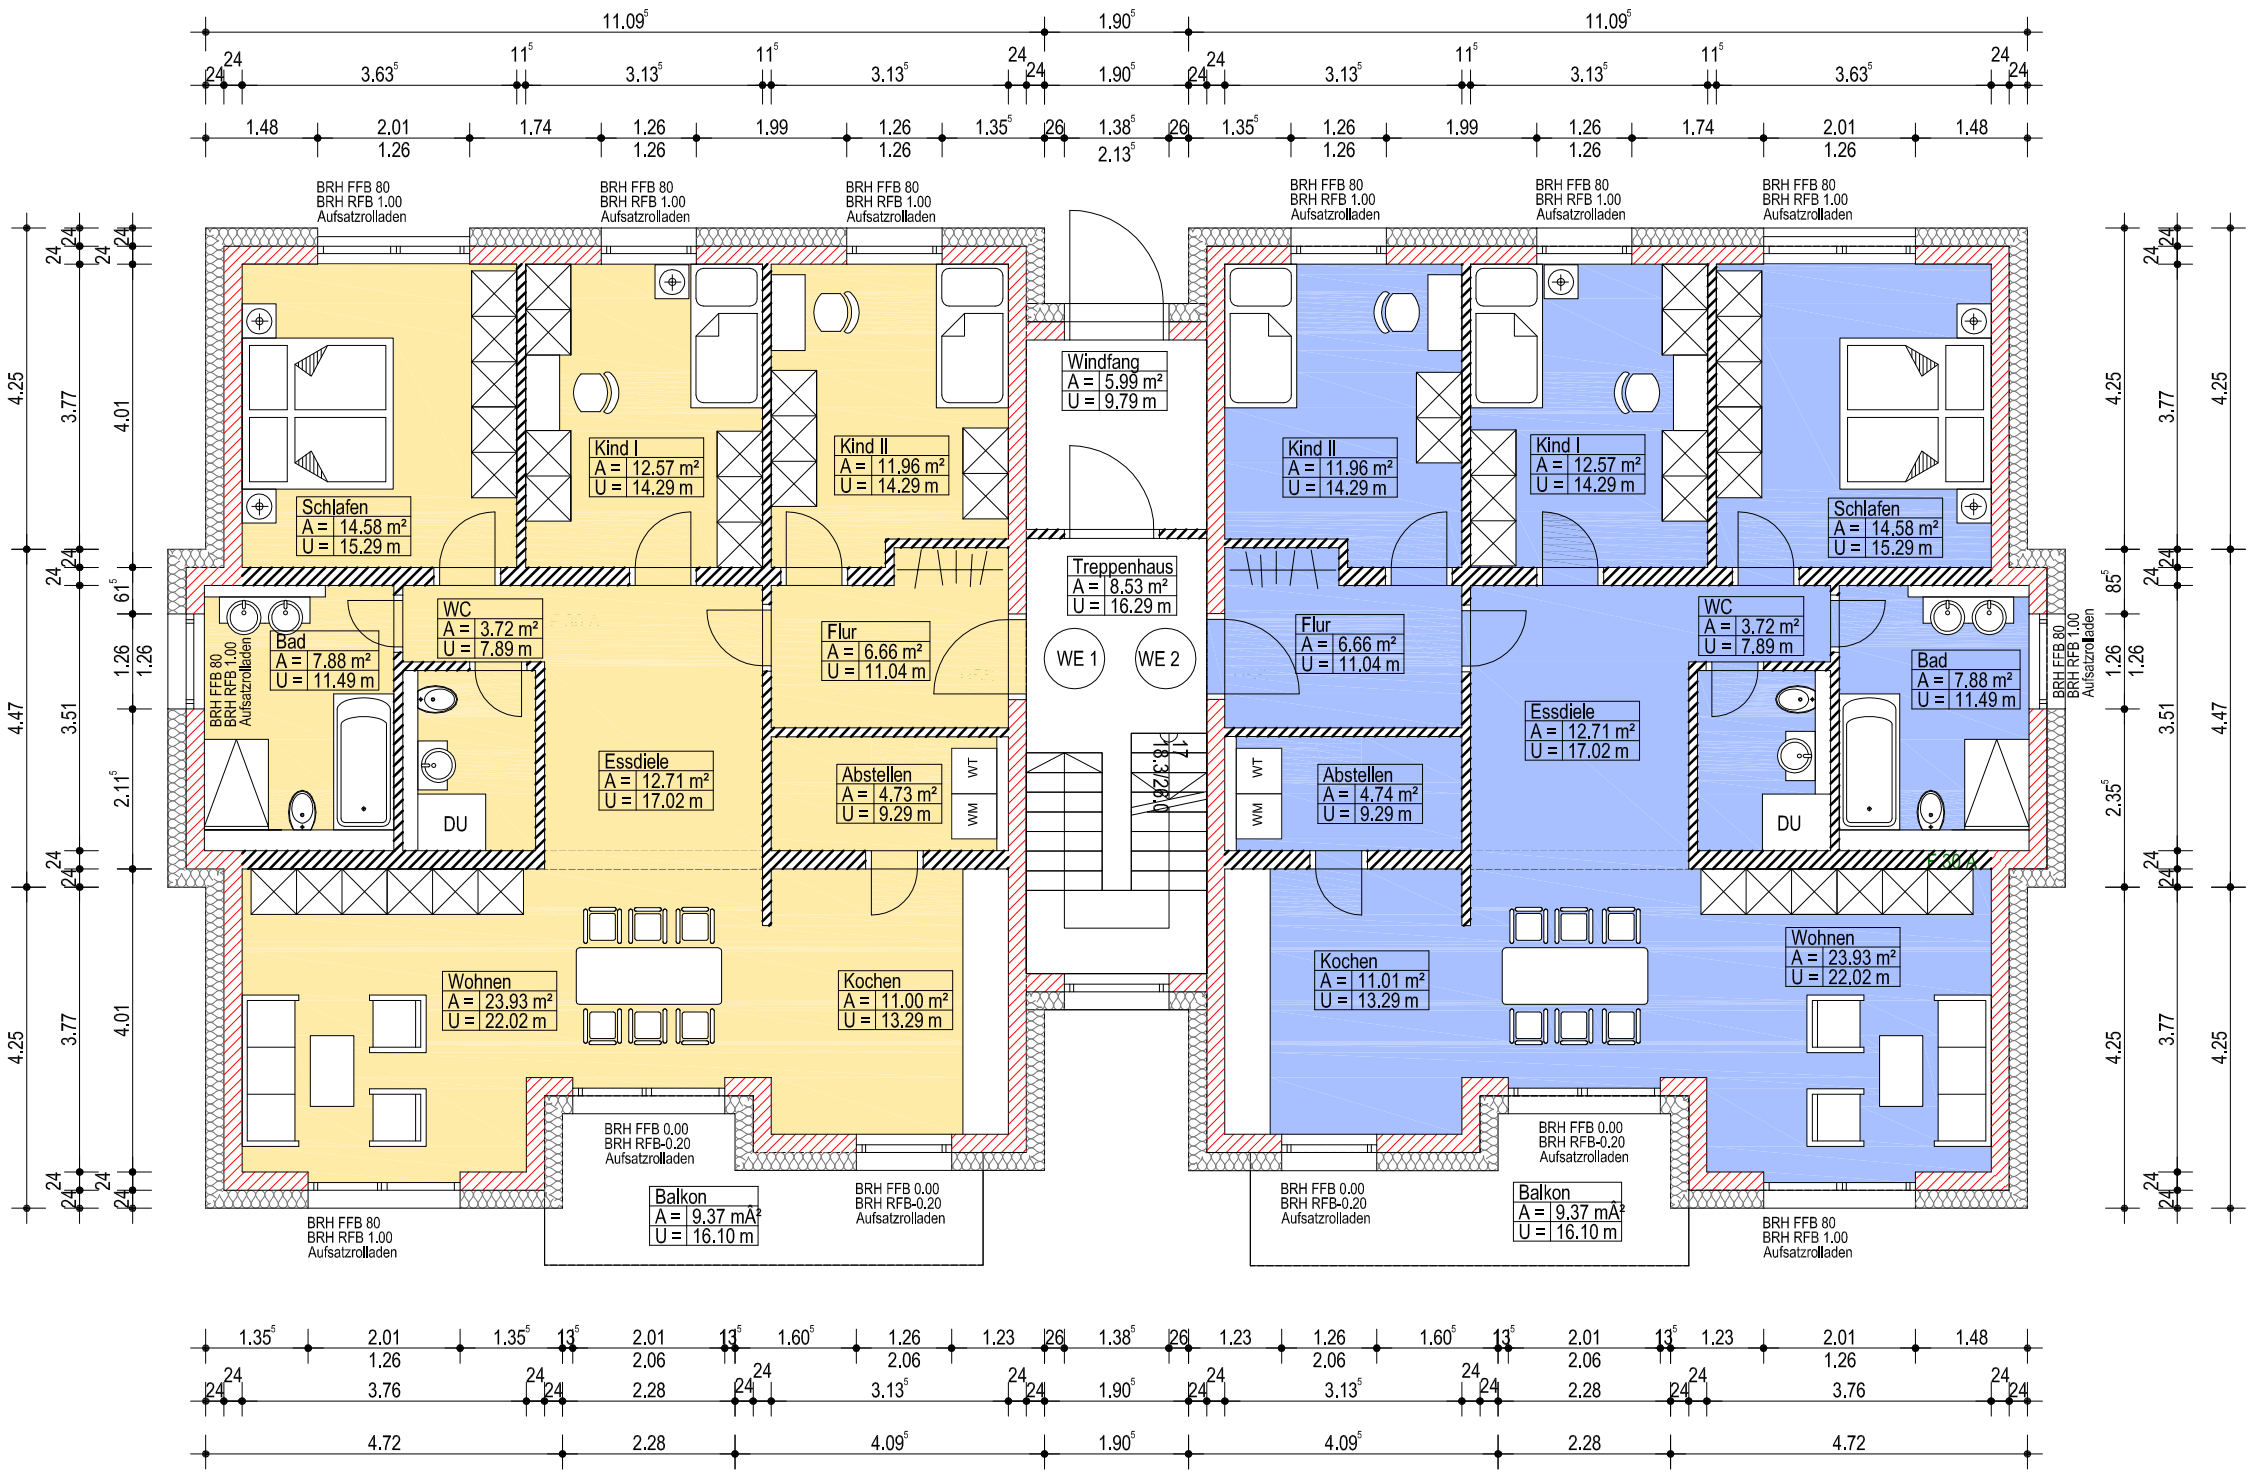

GRUNDRISS ERDGESCHOSS

Diese Zeichnung ist Eigentum der Firma rp gotha gmbh
und darf ohne Genehmigung nicht vervielfältigt,
noch an Dritte weiter gegeben werden.

Dieser Plan gilt nur für die Genehmigungsplanung.
Die vorliegenden Maße und Flächenangaben werden in
der Ausführung konkretisiert.

BAUVORHABEN

Neubau Mehrfamilienwohnhaus
Große Fahnenstrasse 20, 99867 Gotha

PLANUNG
PLANUNGS- U. INGENIEURBÜRO
r p g o t h a g m b h
SCHWABHÄUSER STRASSE 18, 99867 GOTHA
FON: 03621 / 226732
FAX: 03621 / 22699 66 MAIL: info@rp-gotha.de

BAUHERR
HaKa Wohnen GbR
August - Sperl - Straße 12
97355 Castell

UNTERSCHRIFT BAUHERR
.....

PLANUNGSPHASE	GEWERK	INDEX
Genehmigungsplanung	Bauplanung	

PLANBEZEICHNUNG
Grundriss Erdgeschoss

	DATUM	NAME	UNTERSCHRIFT	ZEICHNUNGSNR.	MASSSTAB
BEARBEITET	13.06.2015	Meß		03	M 1 : 100
GEZEICHNET	13.06.2015	Meß			
GEPRÜFT					